



Planta Baixa: Pavimento Térreo

Escala 1:50

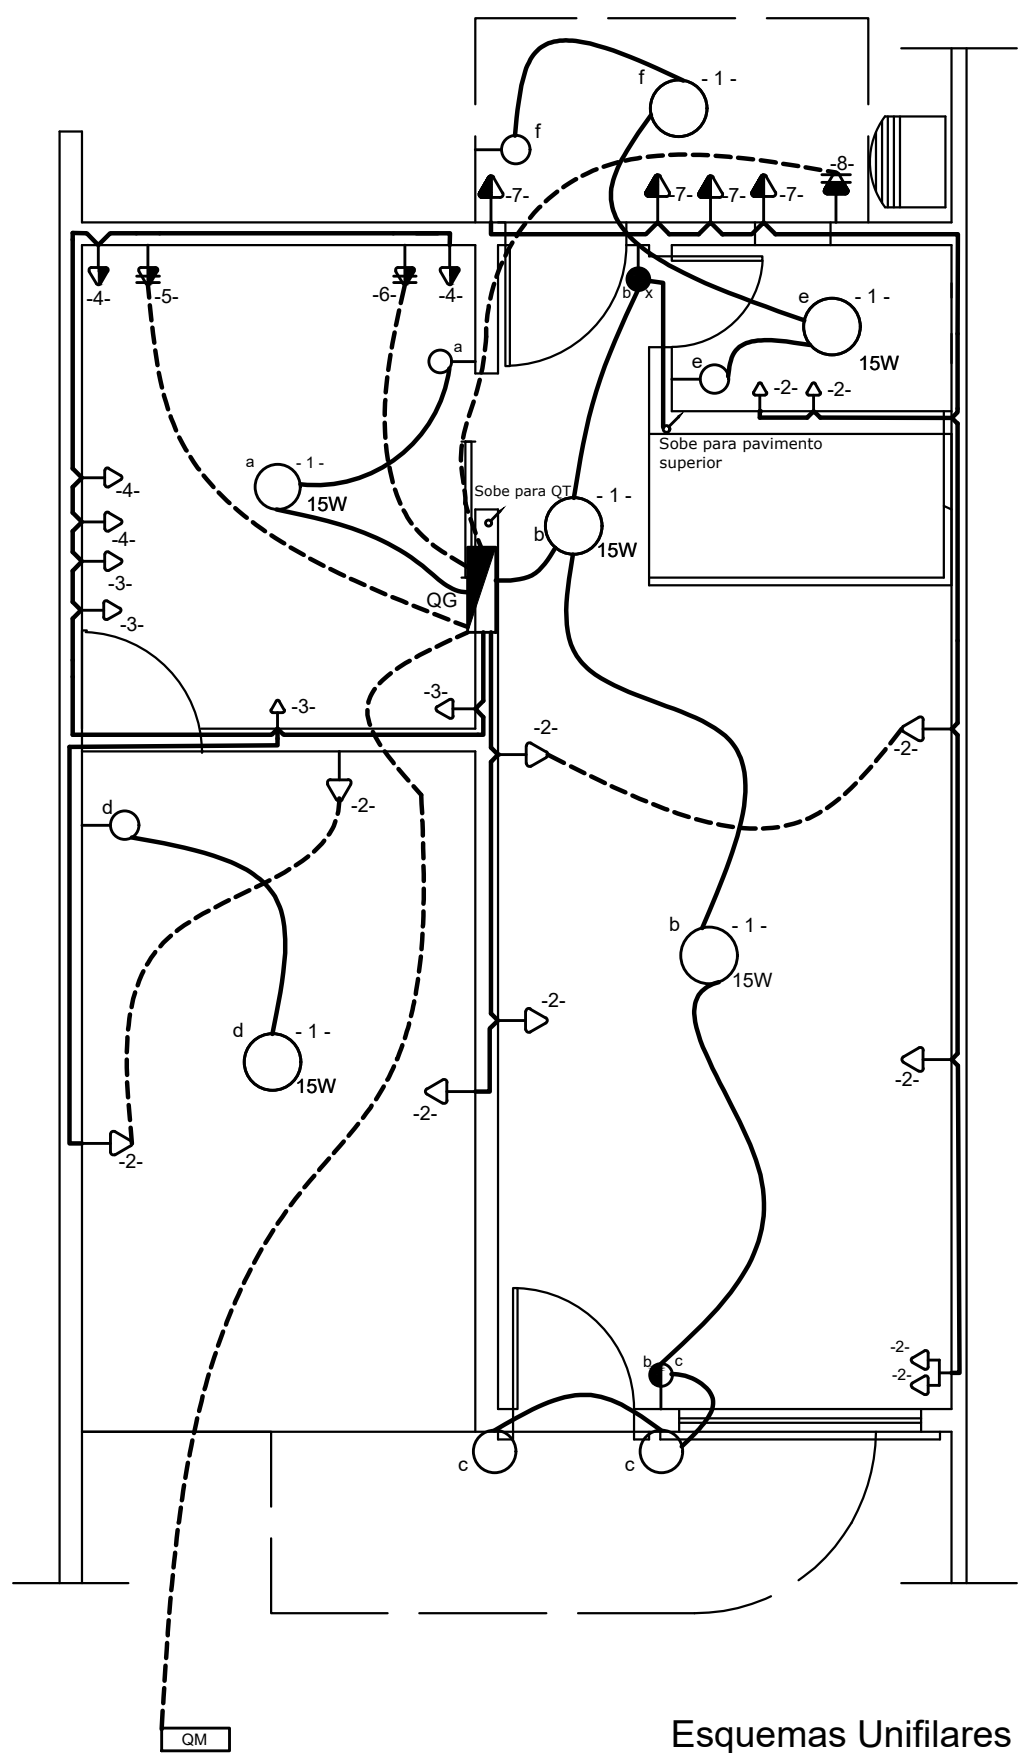


Esquemas Unifilares

Sem escala

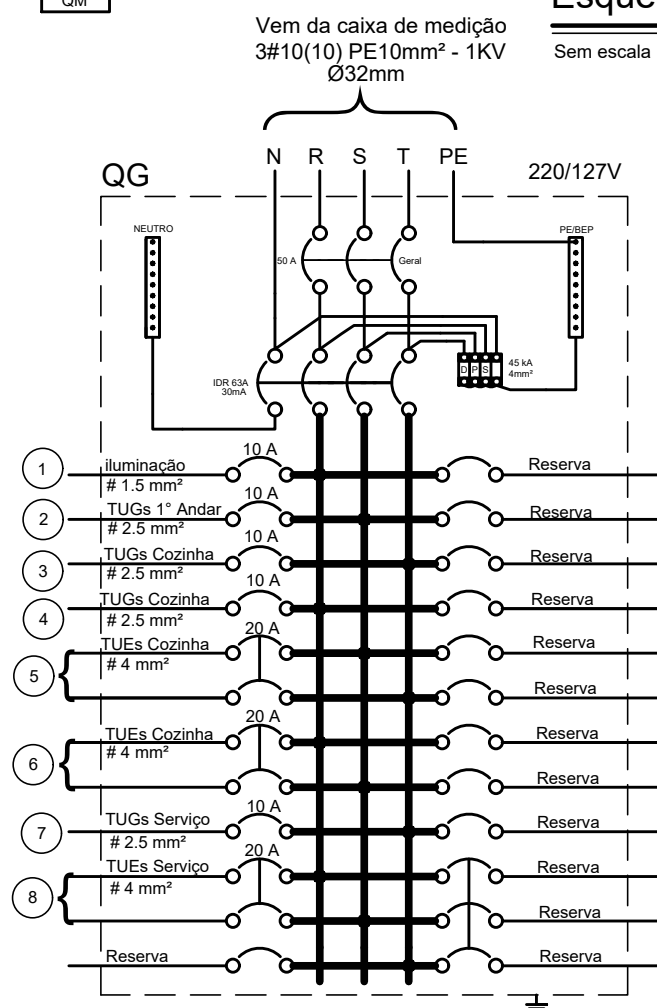


Planta Baixa: Pavimento Superior

Escala 1:50

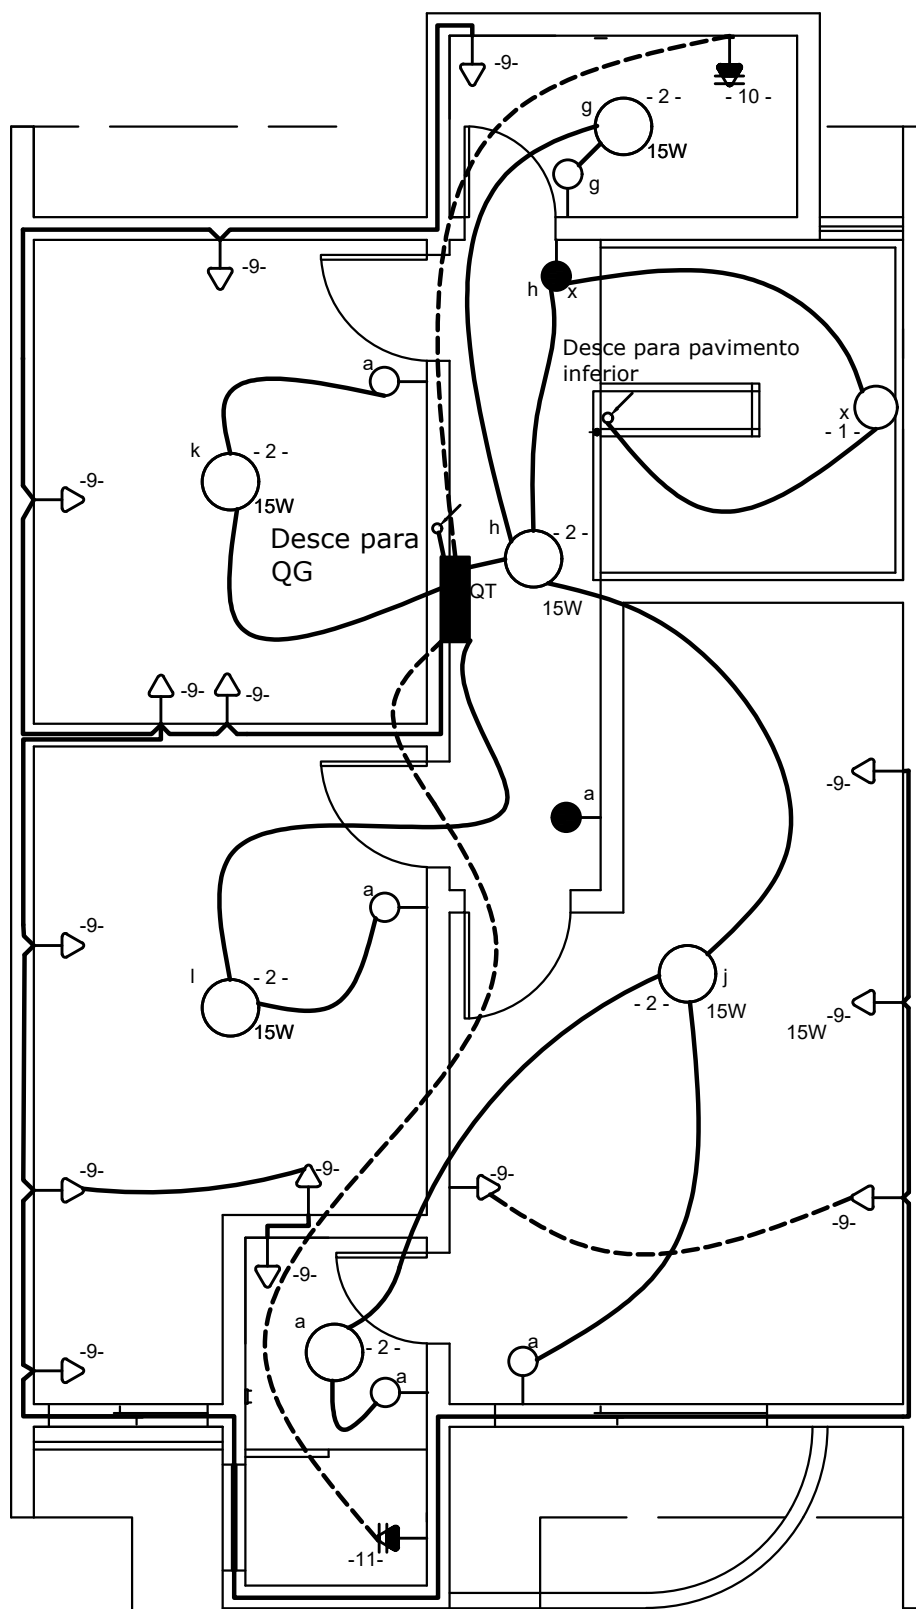

Entrada de Serviço - Padrão COPEL

Sem escala

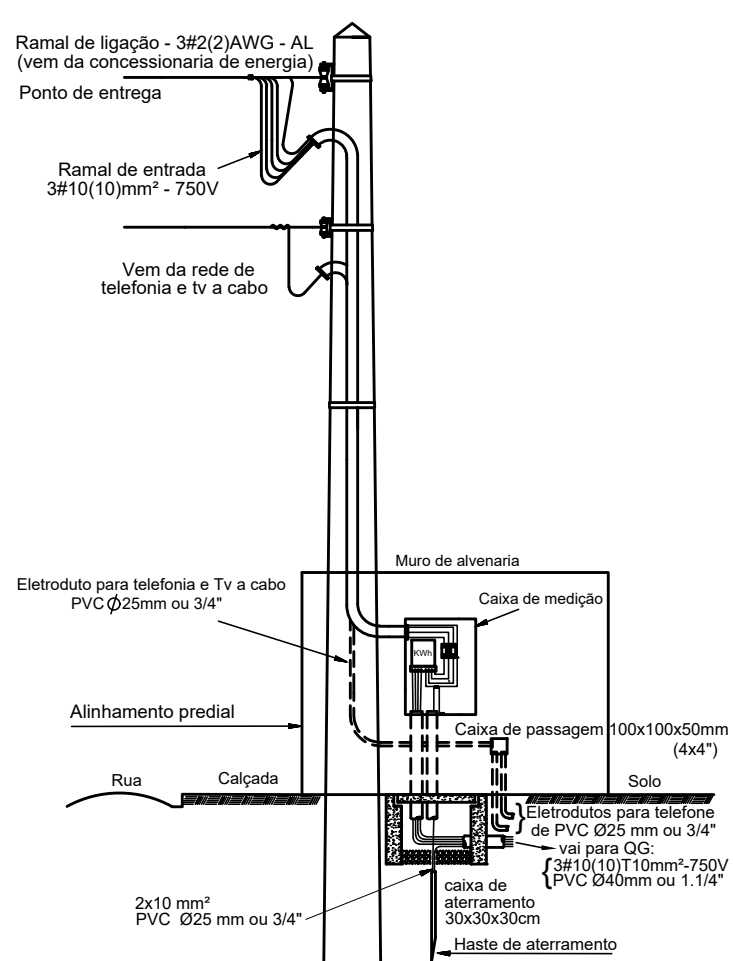

Observações:

1. Qualquer alteração no projeto somente poderá ser feita com a devida autorização do responsável técnico.
2. Todo eletroduto não especificado é de Ø1/2 polegada.
3. Utilizar apenas eletrodutos de PVC 70°
4. Todo cabo não especificado é de seção nominal 1,5 mm².
5. Projeto elaborado em consonância com as normas técnicas NTC-901100, NBR-5410 e NBR-5444
6. Obrigatória a instalação de interruptor diferencial residual (IDR) e dispositivo de proteção contra surto (DPS) conforme especificado no esquema unifilar.

SIMBOLOGIA

(segundo a NBR-5444 - adaptada)

SÍMBOLO	DESCRIÇÃO	
	Tomada 20A baixa (30 cm do piso)	-1- Número do circuito elétrico
	Tomada 20A meia altura (1,30 m do piso)	
	Tomada 20A bifásica alta (220 V)	
	2 tomadas 20A na mesma caixa (30 cm do piso)	
	1 tomada 127V e outra 220V na mesma caixa (30 cm do piso)	
	Interruptor simples (uma tecla)	
	Interruptor paralelo (uma tecla)	
	Interruptor paralelo (duas teclas)	
	Interruptor intermediário	
	Ponto de luz no teto	- 1 - Número do circuito elétrico 15W - Potência da lâmpada a - Comando no interruptor
	Ponto de luz na parede (arandela)	
	Eletroduto que sobe para pavimento superior	
	Eletroduto que desce para pavimento inferior	
	Quadro de Disjuntores (Terminal) - QT	
	Quadro de Disjuntores (Geral) - QG	
	Quadro de Medição (Relógio) - QM	
	Condutores (respectivamente) Neutro, Fase, Retorno e Terra	
	Eletroduto de PVC embutido na alvenaria no teto ou parede	
	Eletroduto de PVC enterrado no solo ou piso	

Reservado ao professor

Revisão (Nome do aluno):

Allan Engel
Arthur

UNIVERSIDADE TECNOLÓGICA FEDERAL DO PARANÁ



DISCIPLINA DE DESENHO ELÉTRICO - PROF. DANIEL JUNGHANS

PROJETO DE INSTALAÇÕES ELÉTRICAS DE UM SOBRADO RESIDENCIAL
PLANTA BAIXA - ESQUEMA UNIFILAR - SIMBOLOGIA - ENTRADA DE SERVIÇO PADRÃO COPEL

DATA
FOLHA
ESCALA
TURMA:
ALUNOS: João Pedro
Guilherme Vidal

30/08/26
1/1
INDICADA
N21