


Planta Baixa: Pavimento Térreo

Escala 1:50

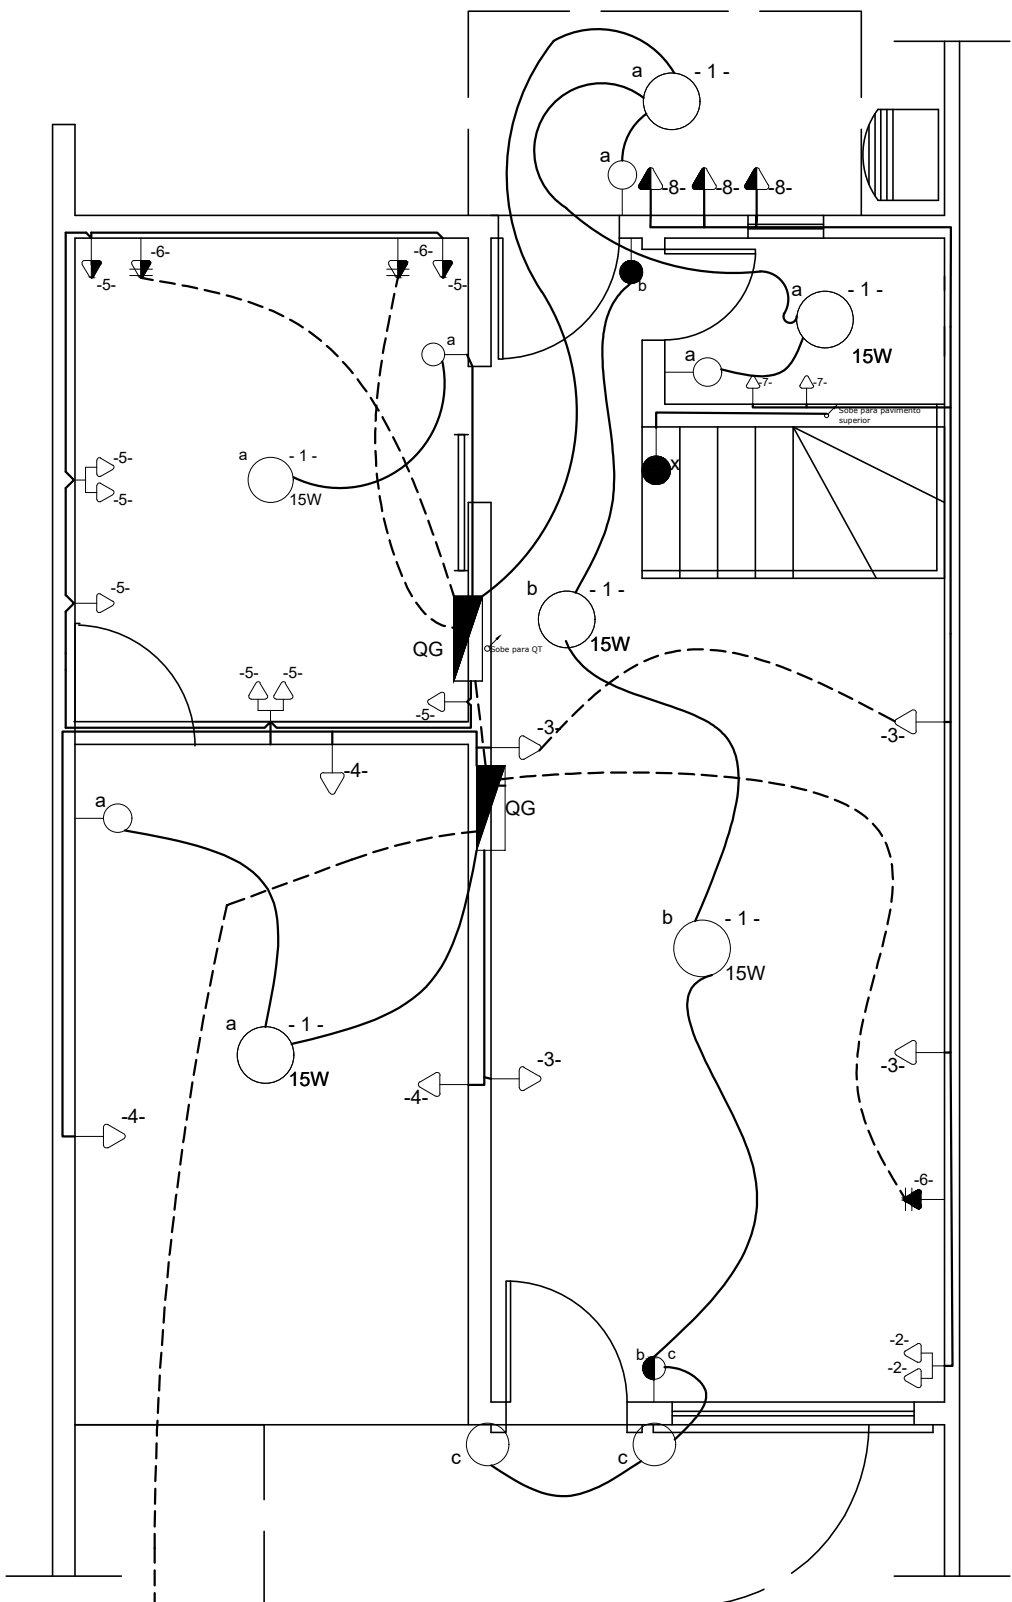


QM


Vem da caixa de medição
3#10(10) PE10mm² - 1KV
Ø32mm

Esquemas Unifilares

Sem escala

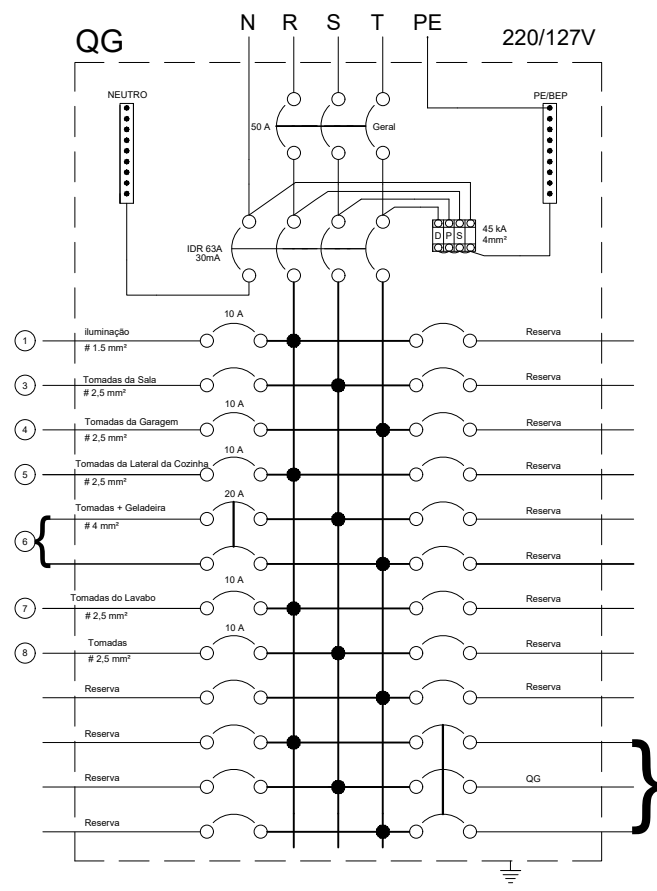


Vem da caixa de medição
3#10(10) PE10mm² - 1KV
Ø32mm

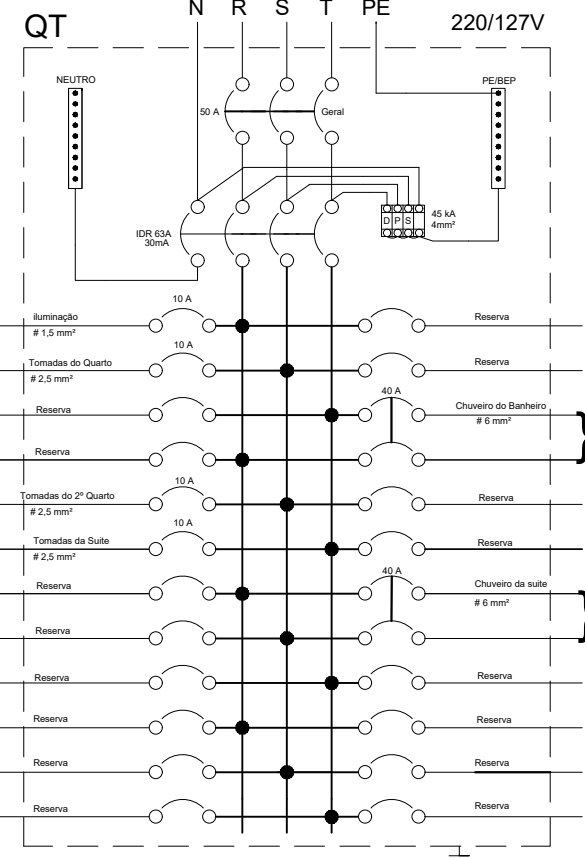


Planta Baixa: Pavimento Superior

Escala 1:50

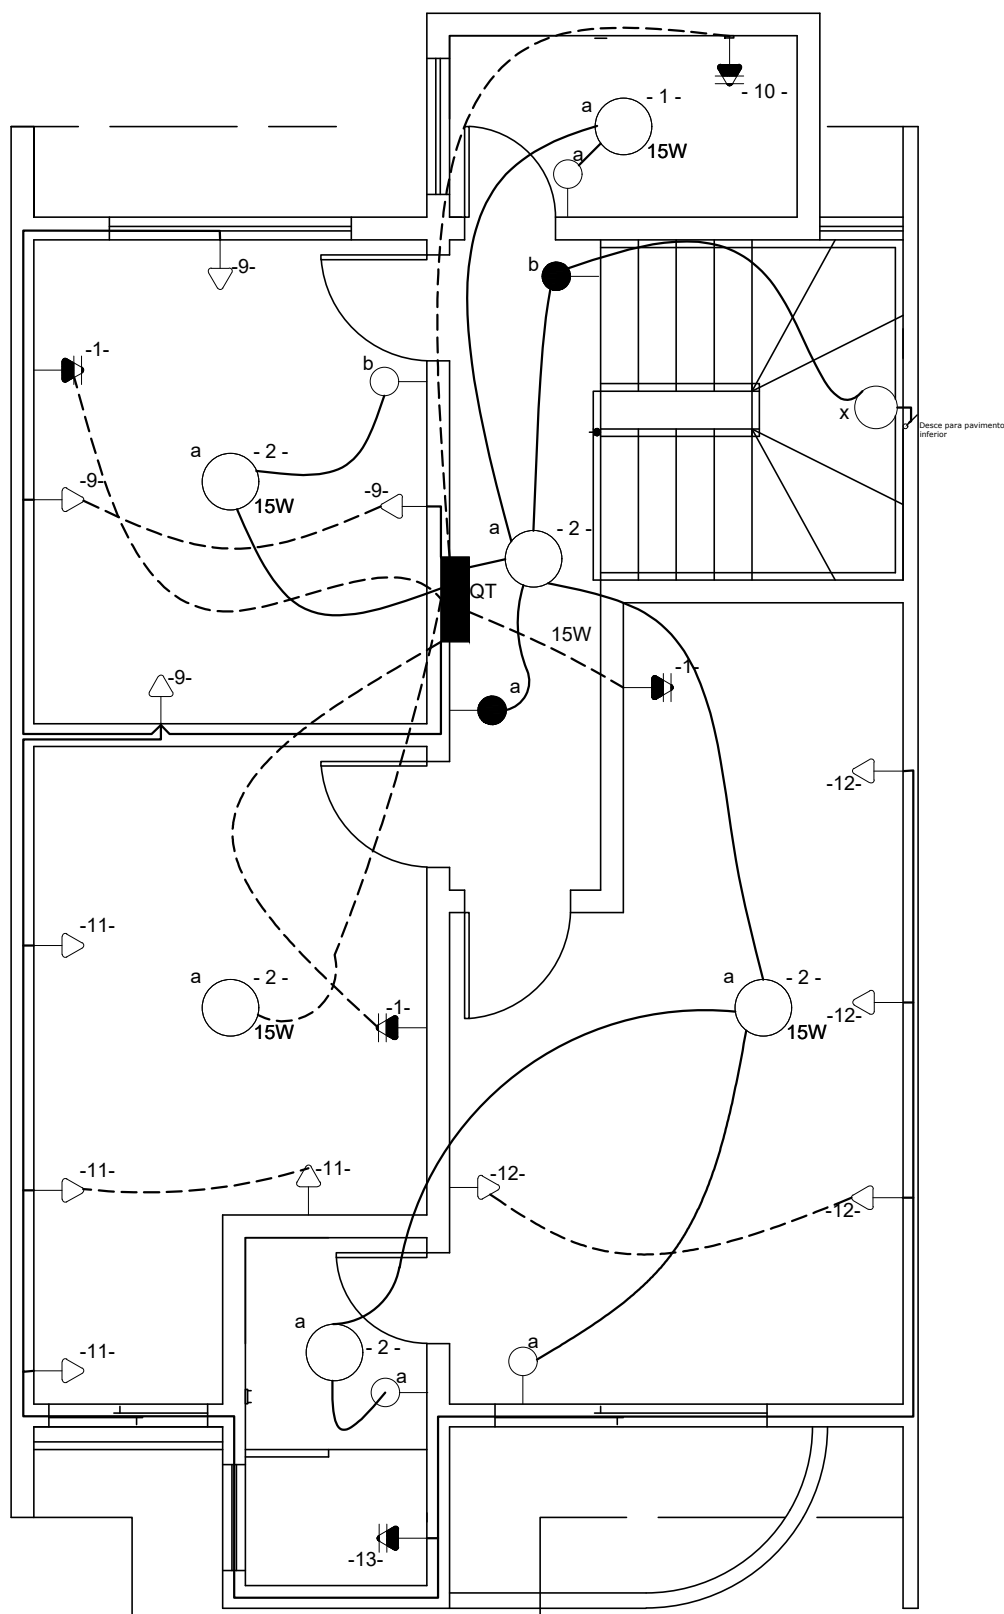

Entrada de Serviço - Padrão COPEL

Sem escala

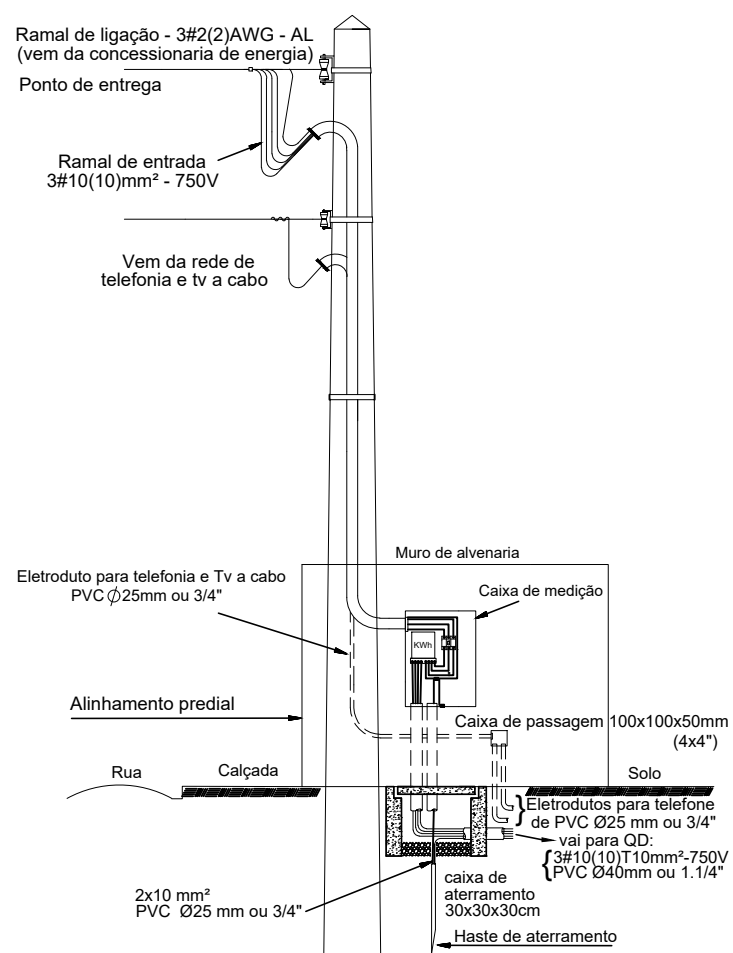

Observações:

1. Qualquer alteração no projeto somente poderá ser feita com a devida autorização do responsável técnico.
2. Todo eletroduto não especificado é de Ø1/2 polegada.
3. Utilizar apenas eletrodutos de PVC 70°
4. Todo cabo não especificado é de seção nominal 1,5 mm².
5. Projeto elaborado em consonância com as normas técnicas NTC-901100, NBR-5410 e NBR-5444
6. Obrigatória a instalação de interruptor diferencial residual (IDR) e dispositivo de proteção contra surto (DPS) conforme especificado no esquema unifilar.

SIMBOLOGIA

(segundo a NBR-5444 - adaptada)

SÍMBOLO	DESCRIÇÃO
	Tomada 20A baixa (30 cm do piso)
	Tomada 20A meia altura (1,30 m do piso)
	Tomada 20A bifásica alta (220 V)
	2 tomadas 20A na mesma caixa (30 cm do piso)
	1 tomada 127V e outra 220V na mesma caixa (30 cm do piso)
	Interruptor simples (uma tecla)
	Interruptor paralelo (uma tecla)
	Interruptor intermediário
	Ponto de luz no teto
	Ponto de luz na parede (arandela)
	Eletroduto que sobe para pavimento superior
	Eletroduto que desce para pavimento inferior
	Quadro de Disjuntores (Terminal) - QT
	Quadro de Disjuntores (Geral) - QG
	Quadro de Medição (Relógio) - QM
	Condutores (respectivamente) Neutro, Fase, Retorno e Terra
	Eletroduto de PVC embutido na alvenaria no teto ou parede
	Eletroduto de PVC enterrado no solo ou piso

Reservado ao professor

Revisão (Nome do aluno):

UNIVERSIDADE TECNOLÓGICA FEDERAL DO PARANÁ

UTPR

DISCIPLINA DE DESENHO ELÉTRICO - PROF. DANIEL JUNGHANS

PROJETO DE INSTALAÇÕES ELÉTRICAS DE UM SOBRADO RESIDENCIAL
PLANTA BAIXA - ESQUEMA UNIFILAR - SIMBOLOGIA - ENTRADA DE SERVIÇO PADRÃO COPEL

DATA	/ /
FOLHA	1/1
ESCALA	INDICADA
TURMA	S
ALUNOS:	